03 Thriving Lingnan village

Combination of Traditional Lingnan Architectural Elements and Science & Technology Museums


Location: Zengcheng District, Guangzhou, China
Date: Jul 2023 - Aug 2023
Instructor: Dr. Fengdeng Wan, Dr. Mingbo Xi
Acadamic Work: College Recommended Competitions, Group Work

The project participated in the **2024 International Solar Building Design Competition** on the topic of designing Zengcheng Science & Technology Museum.


I was in charge of the preliminary analysis, the development of the program, the green and energy-saving design and carbon calculations, floor plans, detail drawings, analytical drawings, and the production of renderings.



Idea

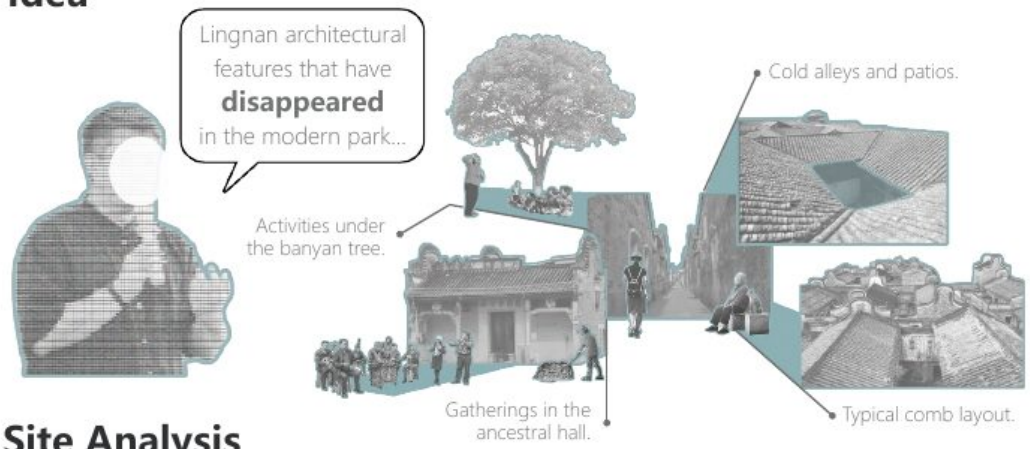


Block Generation

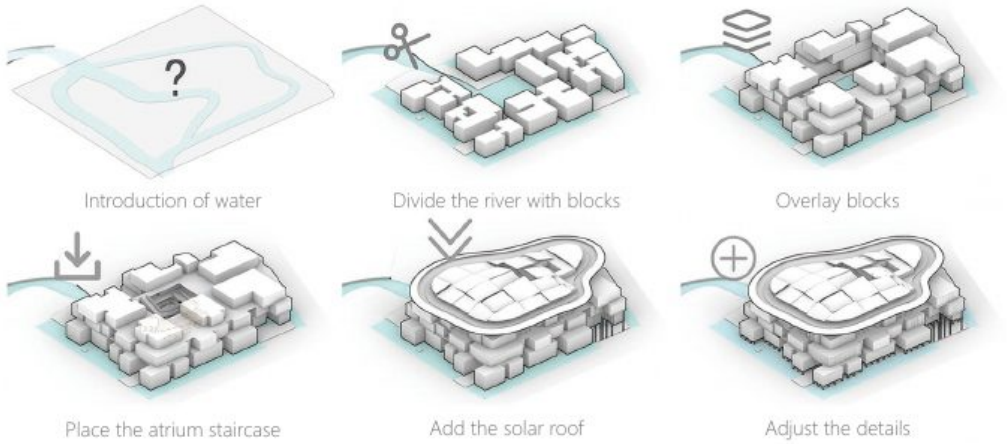


Site Analysis




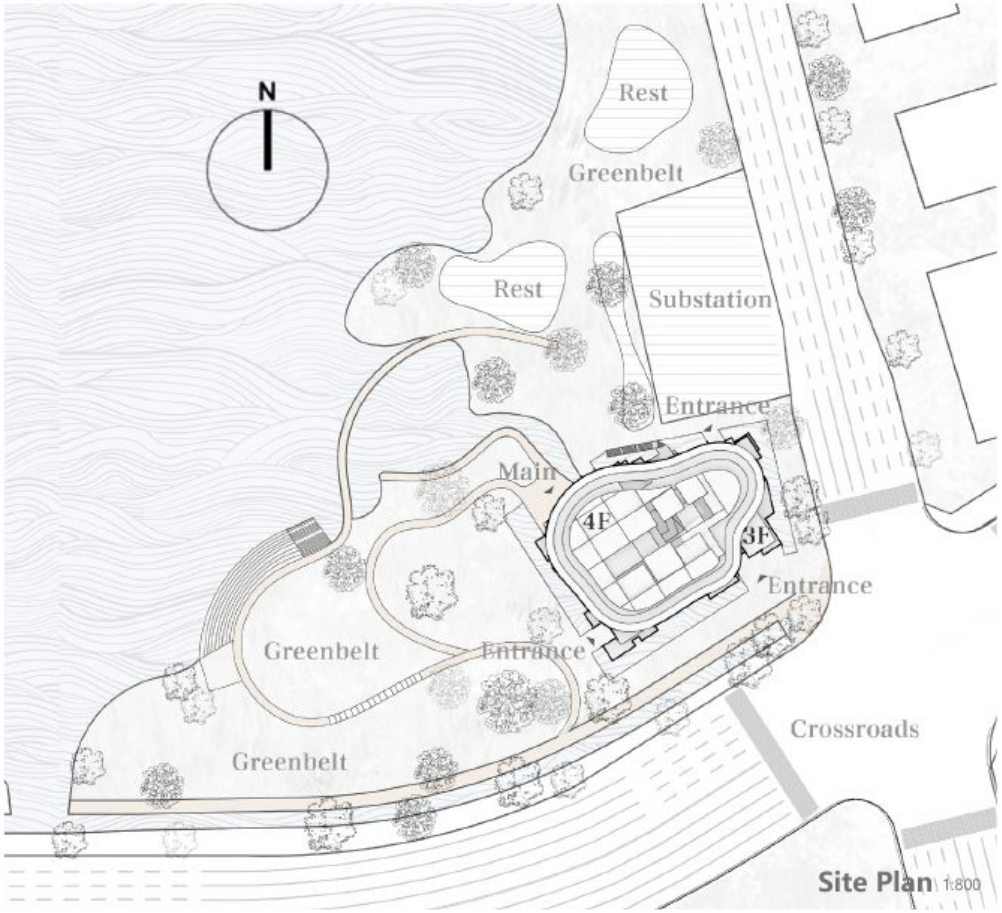



Energy-saving System

detailed introduction of nodes on water recycling and sunshine energy utilization

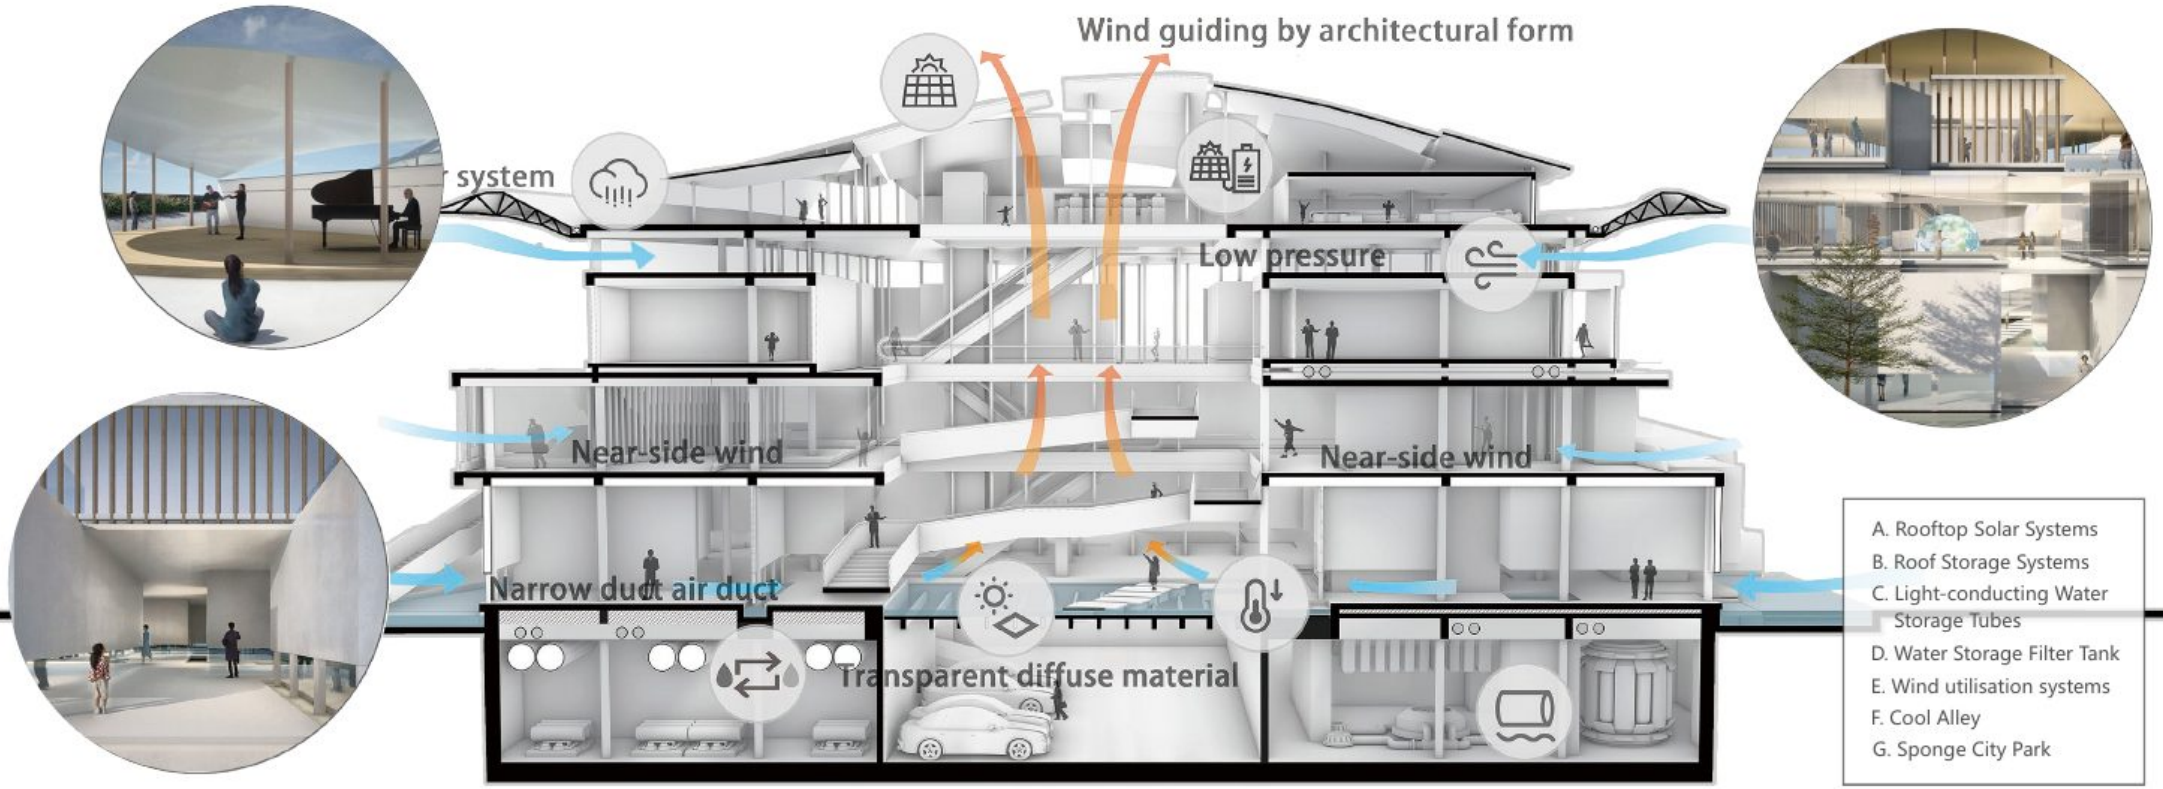

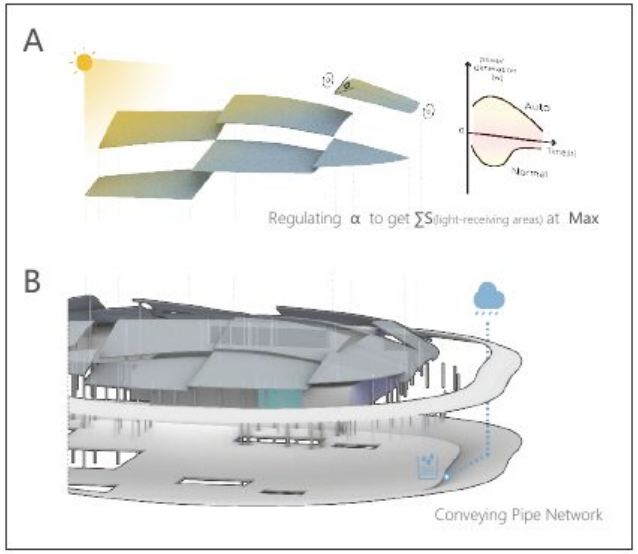


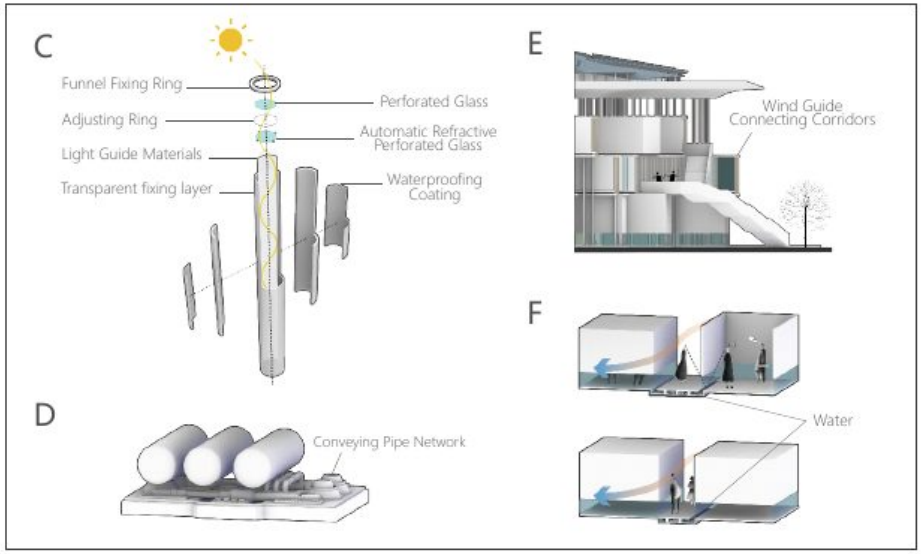

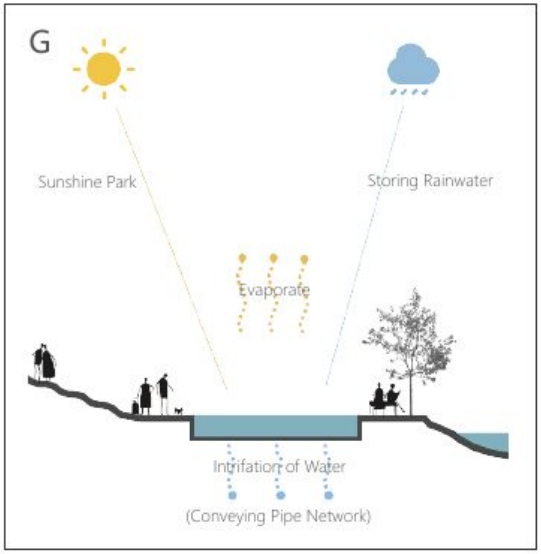







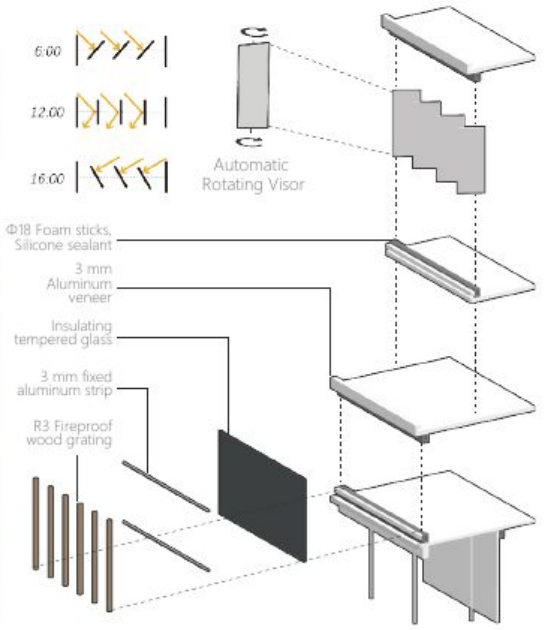


Glass Wall Details

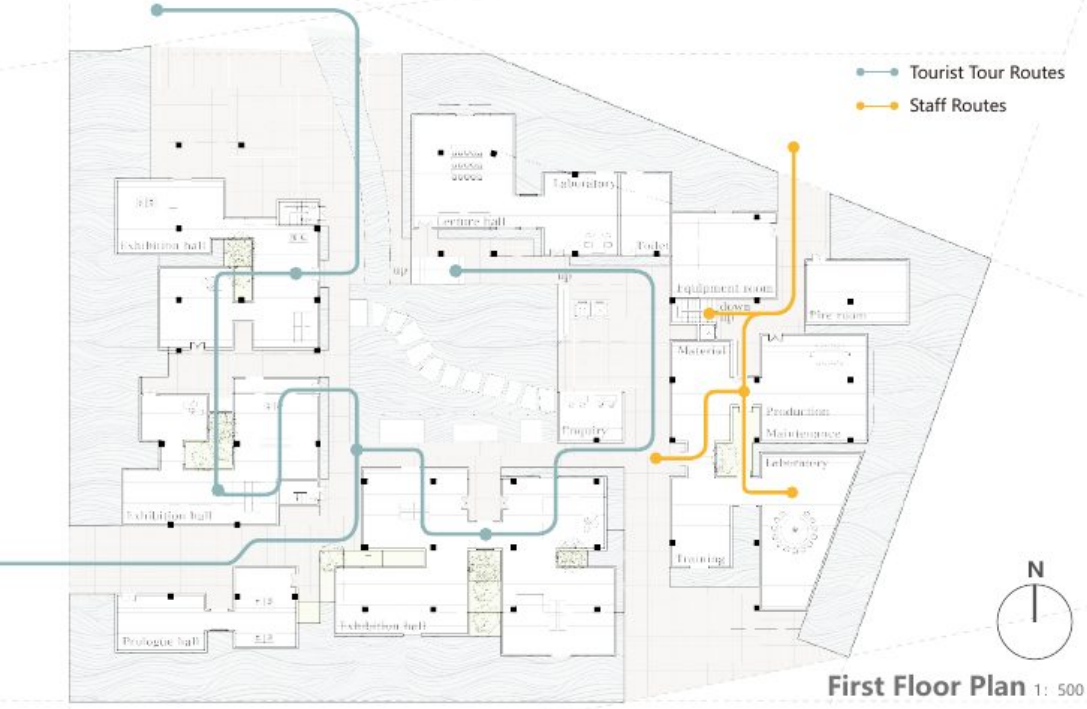

First Floor Plan 1: 500

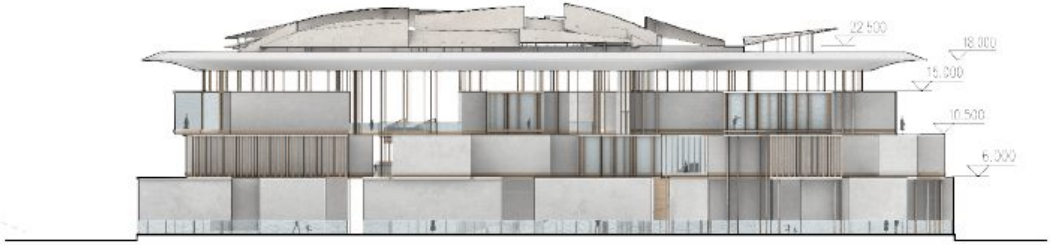

South Facade 1:500

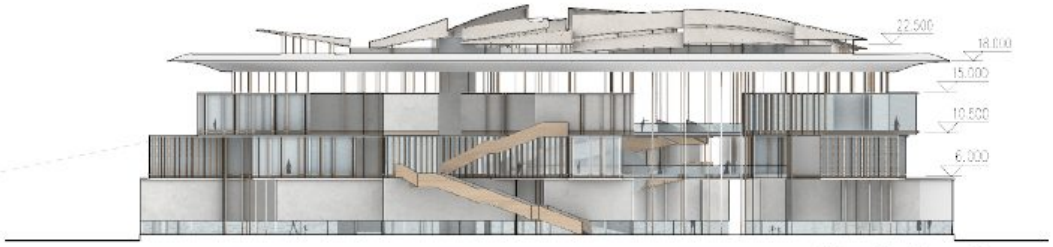

North Facade 1:500



In southern mist and rain, the sky sinks low, Beneath thick shade, the banyan trees grow.

The pond's surface stirs with a gentle sway, By the alley's mouth, white gulls find their way.

- Southern Water Village at Dusk -